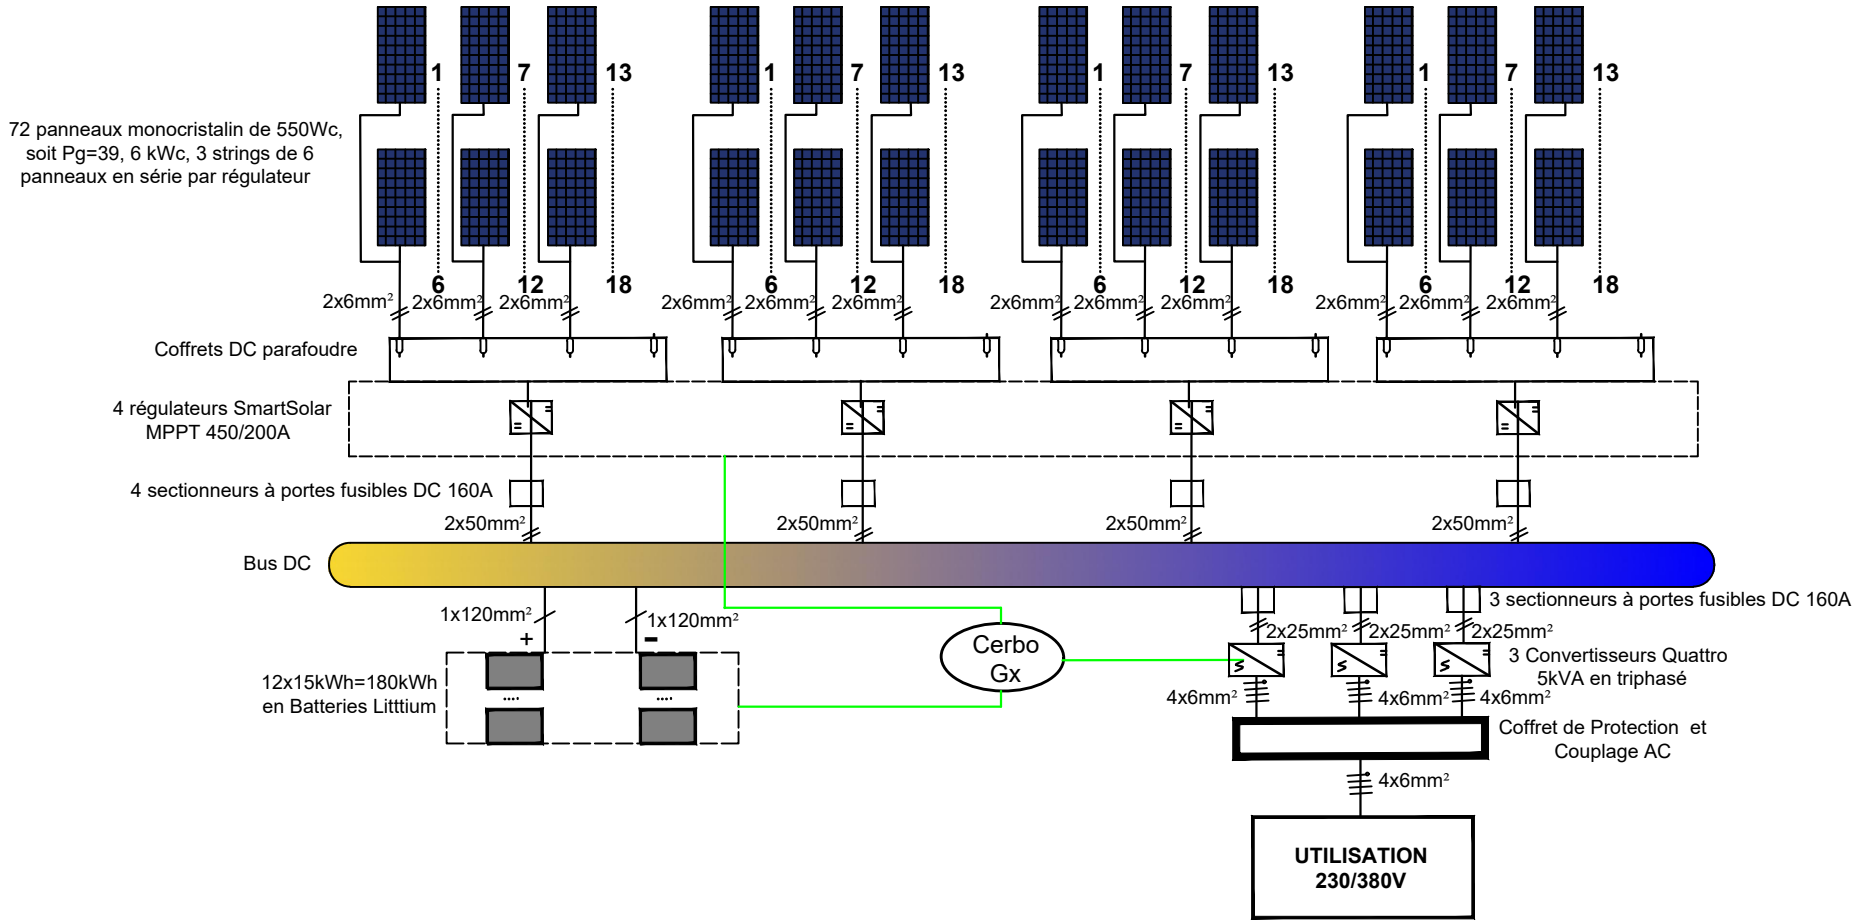


Titre	Projet Solaire de la boulangerie YORO de Manantali	Date : Le 07 mars 2026
Description	Schéma unifilaire du système d'énergie solaire	Dessiné M. Simaro DEMBELE